


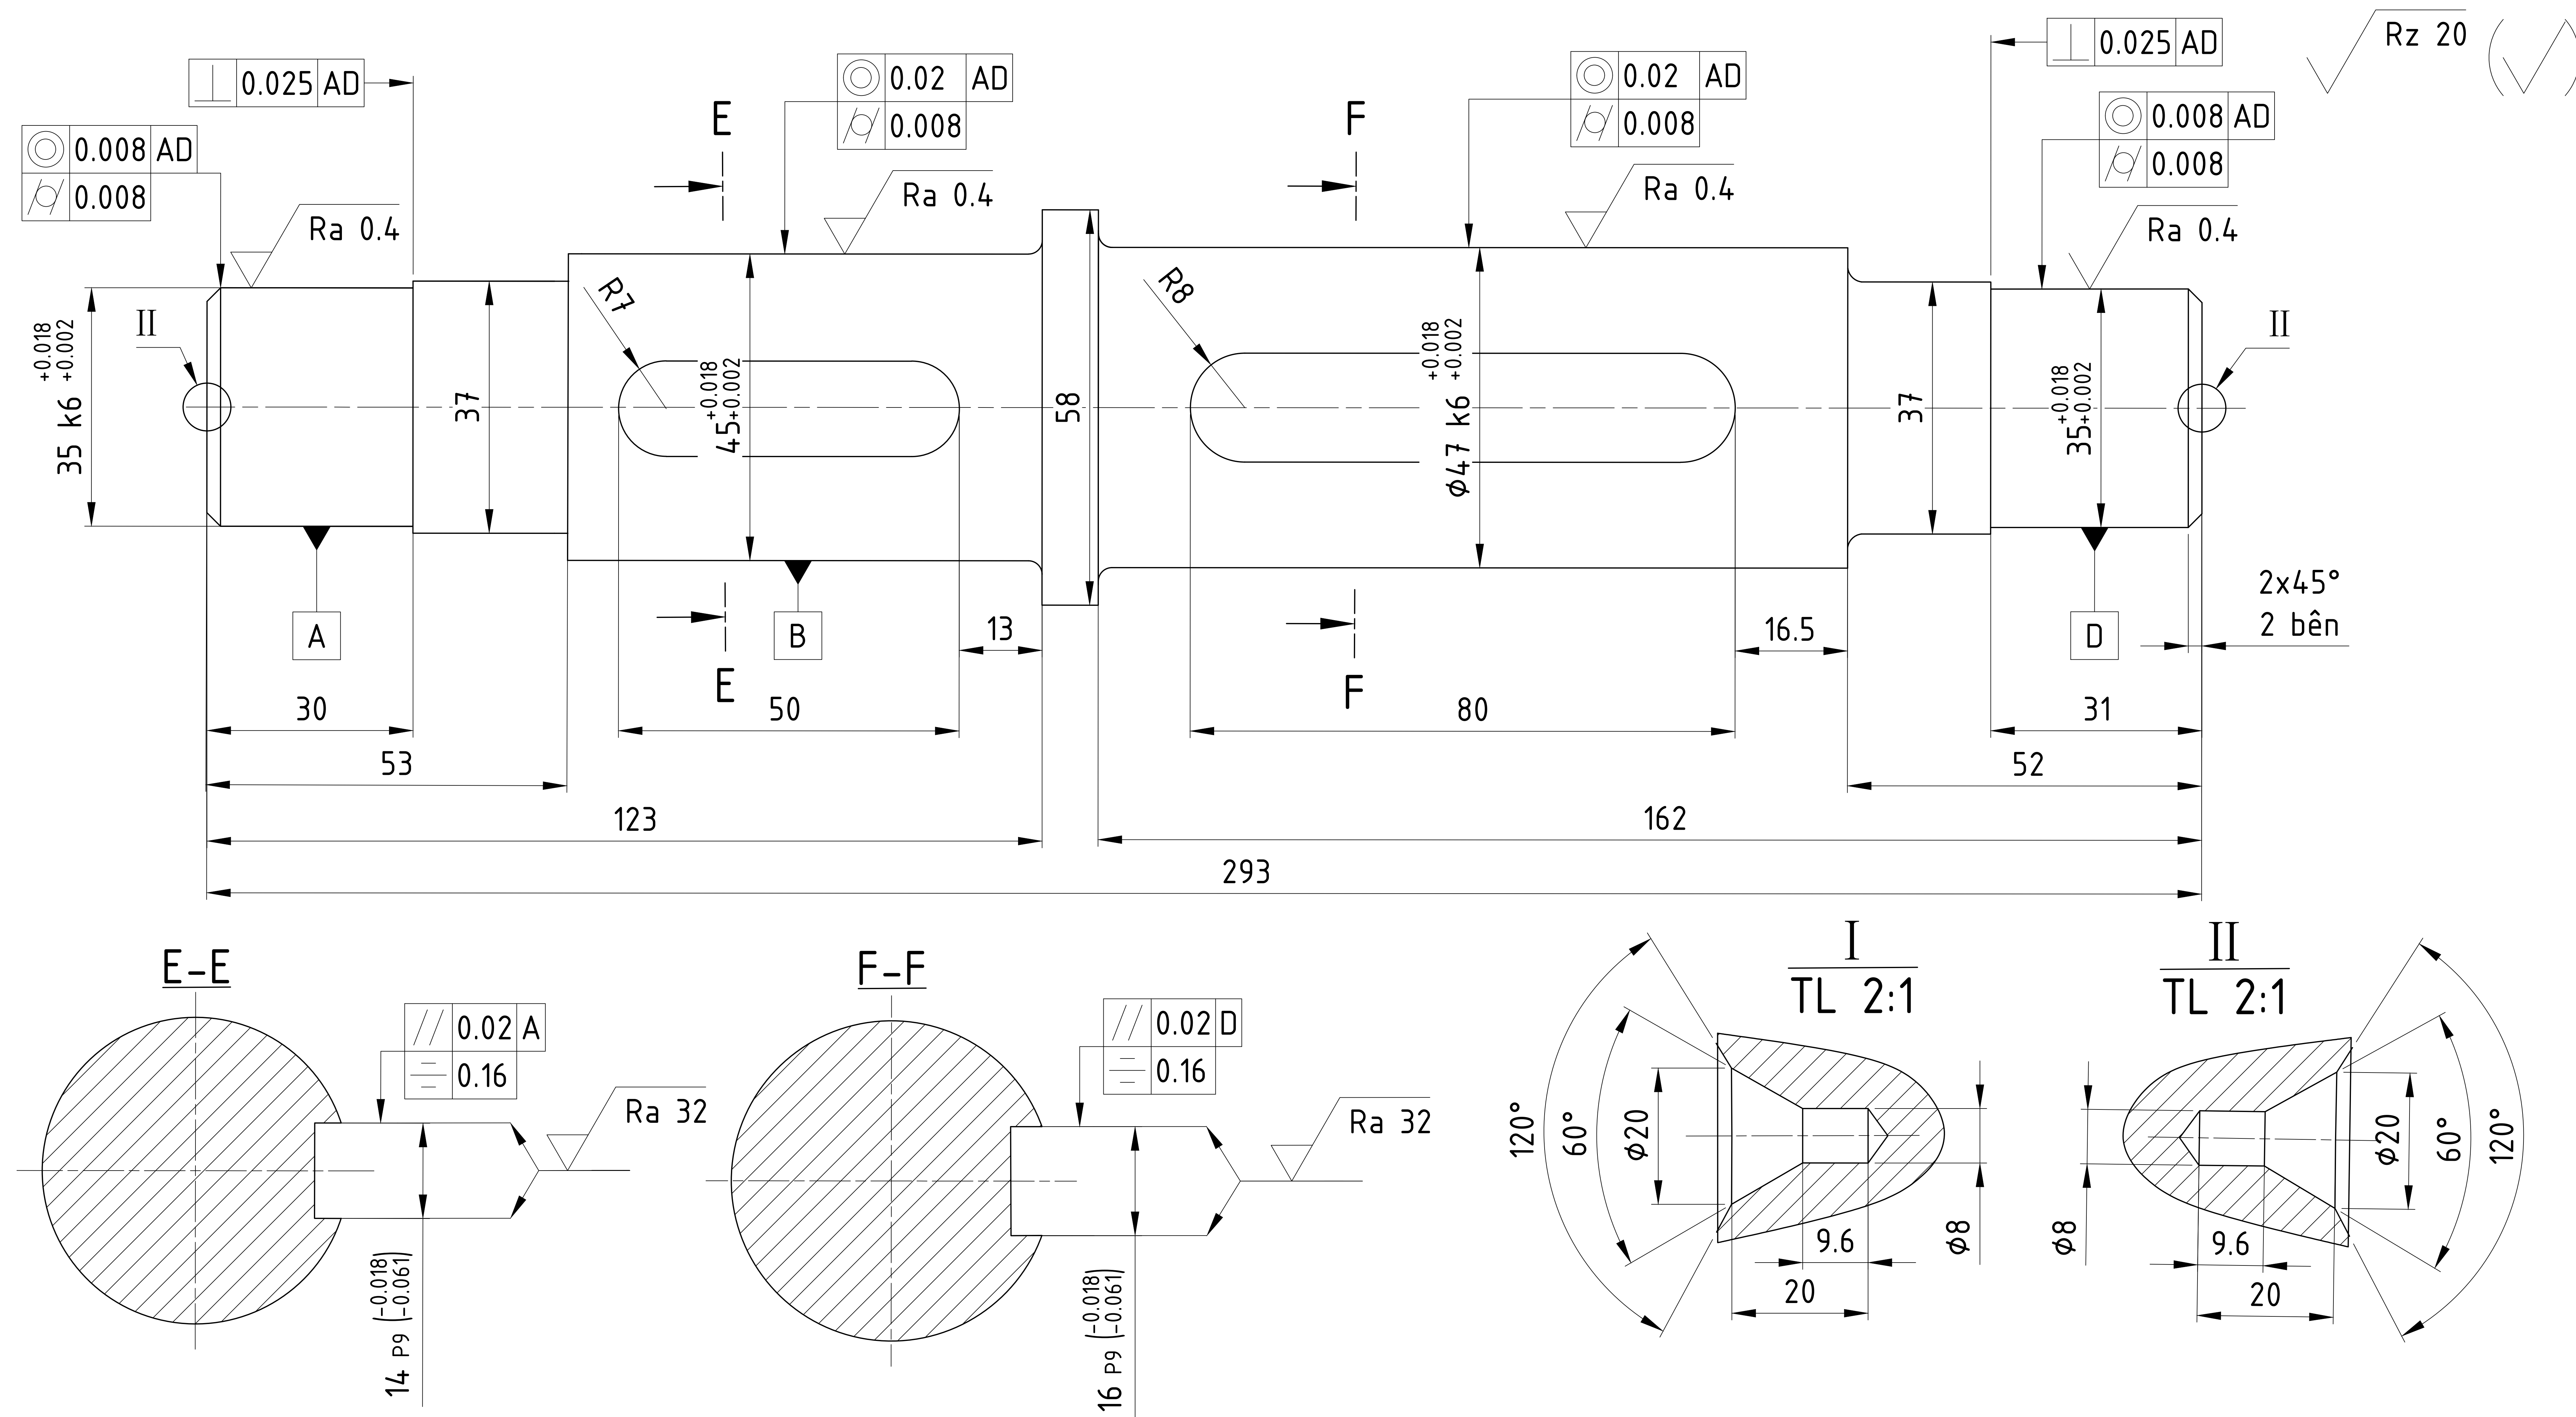

- Yêu cầu kỹ thuật:**
- Nhiệt luyện: Tôi cải thiện HB192...240.
  - Sai lệch giới hạn của các kích thước không chỉ dẫn: mặt bao H14, mặt bị bao h14, còn lại  $\pm IT_{\frac{14}{2}}$ .
  - Làm sạch trục, làm cùn góc, cạnh sắc.

|                                               |                                   |                |                     |                 |                |                            |
|-----------------------------------------------|-----------------------------------|----------------|---------------------|-----------------|----------------|----------------------------|
| ĐHQG TP.HCM<br>Trường ĐH Bách khoa<br>(HCMUT) | Khoa Cơ khí – Bộ môn Thiết kế máy |                | HK251               |                 |                |                            |
|                                               | ĐỒ ÁN THIẾT KẾ                    |                | TP.HCM              |                 |                |                            |
| THIẾT KẾ HỆ THỐNG DẪN ĐỘNG XÍCH TẢI           |                                   |                |                     |                 |                |                            |
| Chức danh                                     | Chữ ký                            | Họ và tên      | TRỤC II<br>Thép C45 | Tỉ lệ           | Hội đồng: .... |                            |
| Sinh viên                                     |                                   | Trần Minh Đức  |                     | 1:1             |                |                            |
|                                               |                                   |                |                     | Tờ số / số tờ   | Khối lượng, kg |                            |
| GVHD                                          |                                   | Phạm Minh Tuấn |                     | /               |                |                            |
| GVPB                                          |                                   |                |                     | Ngày hoàn thành | 05/12/2025     | Ngày bảo vệ:    /    /2025 |